


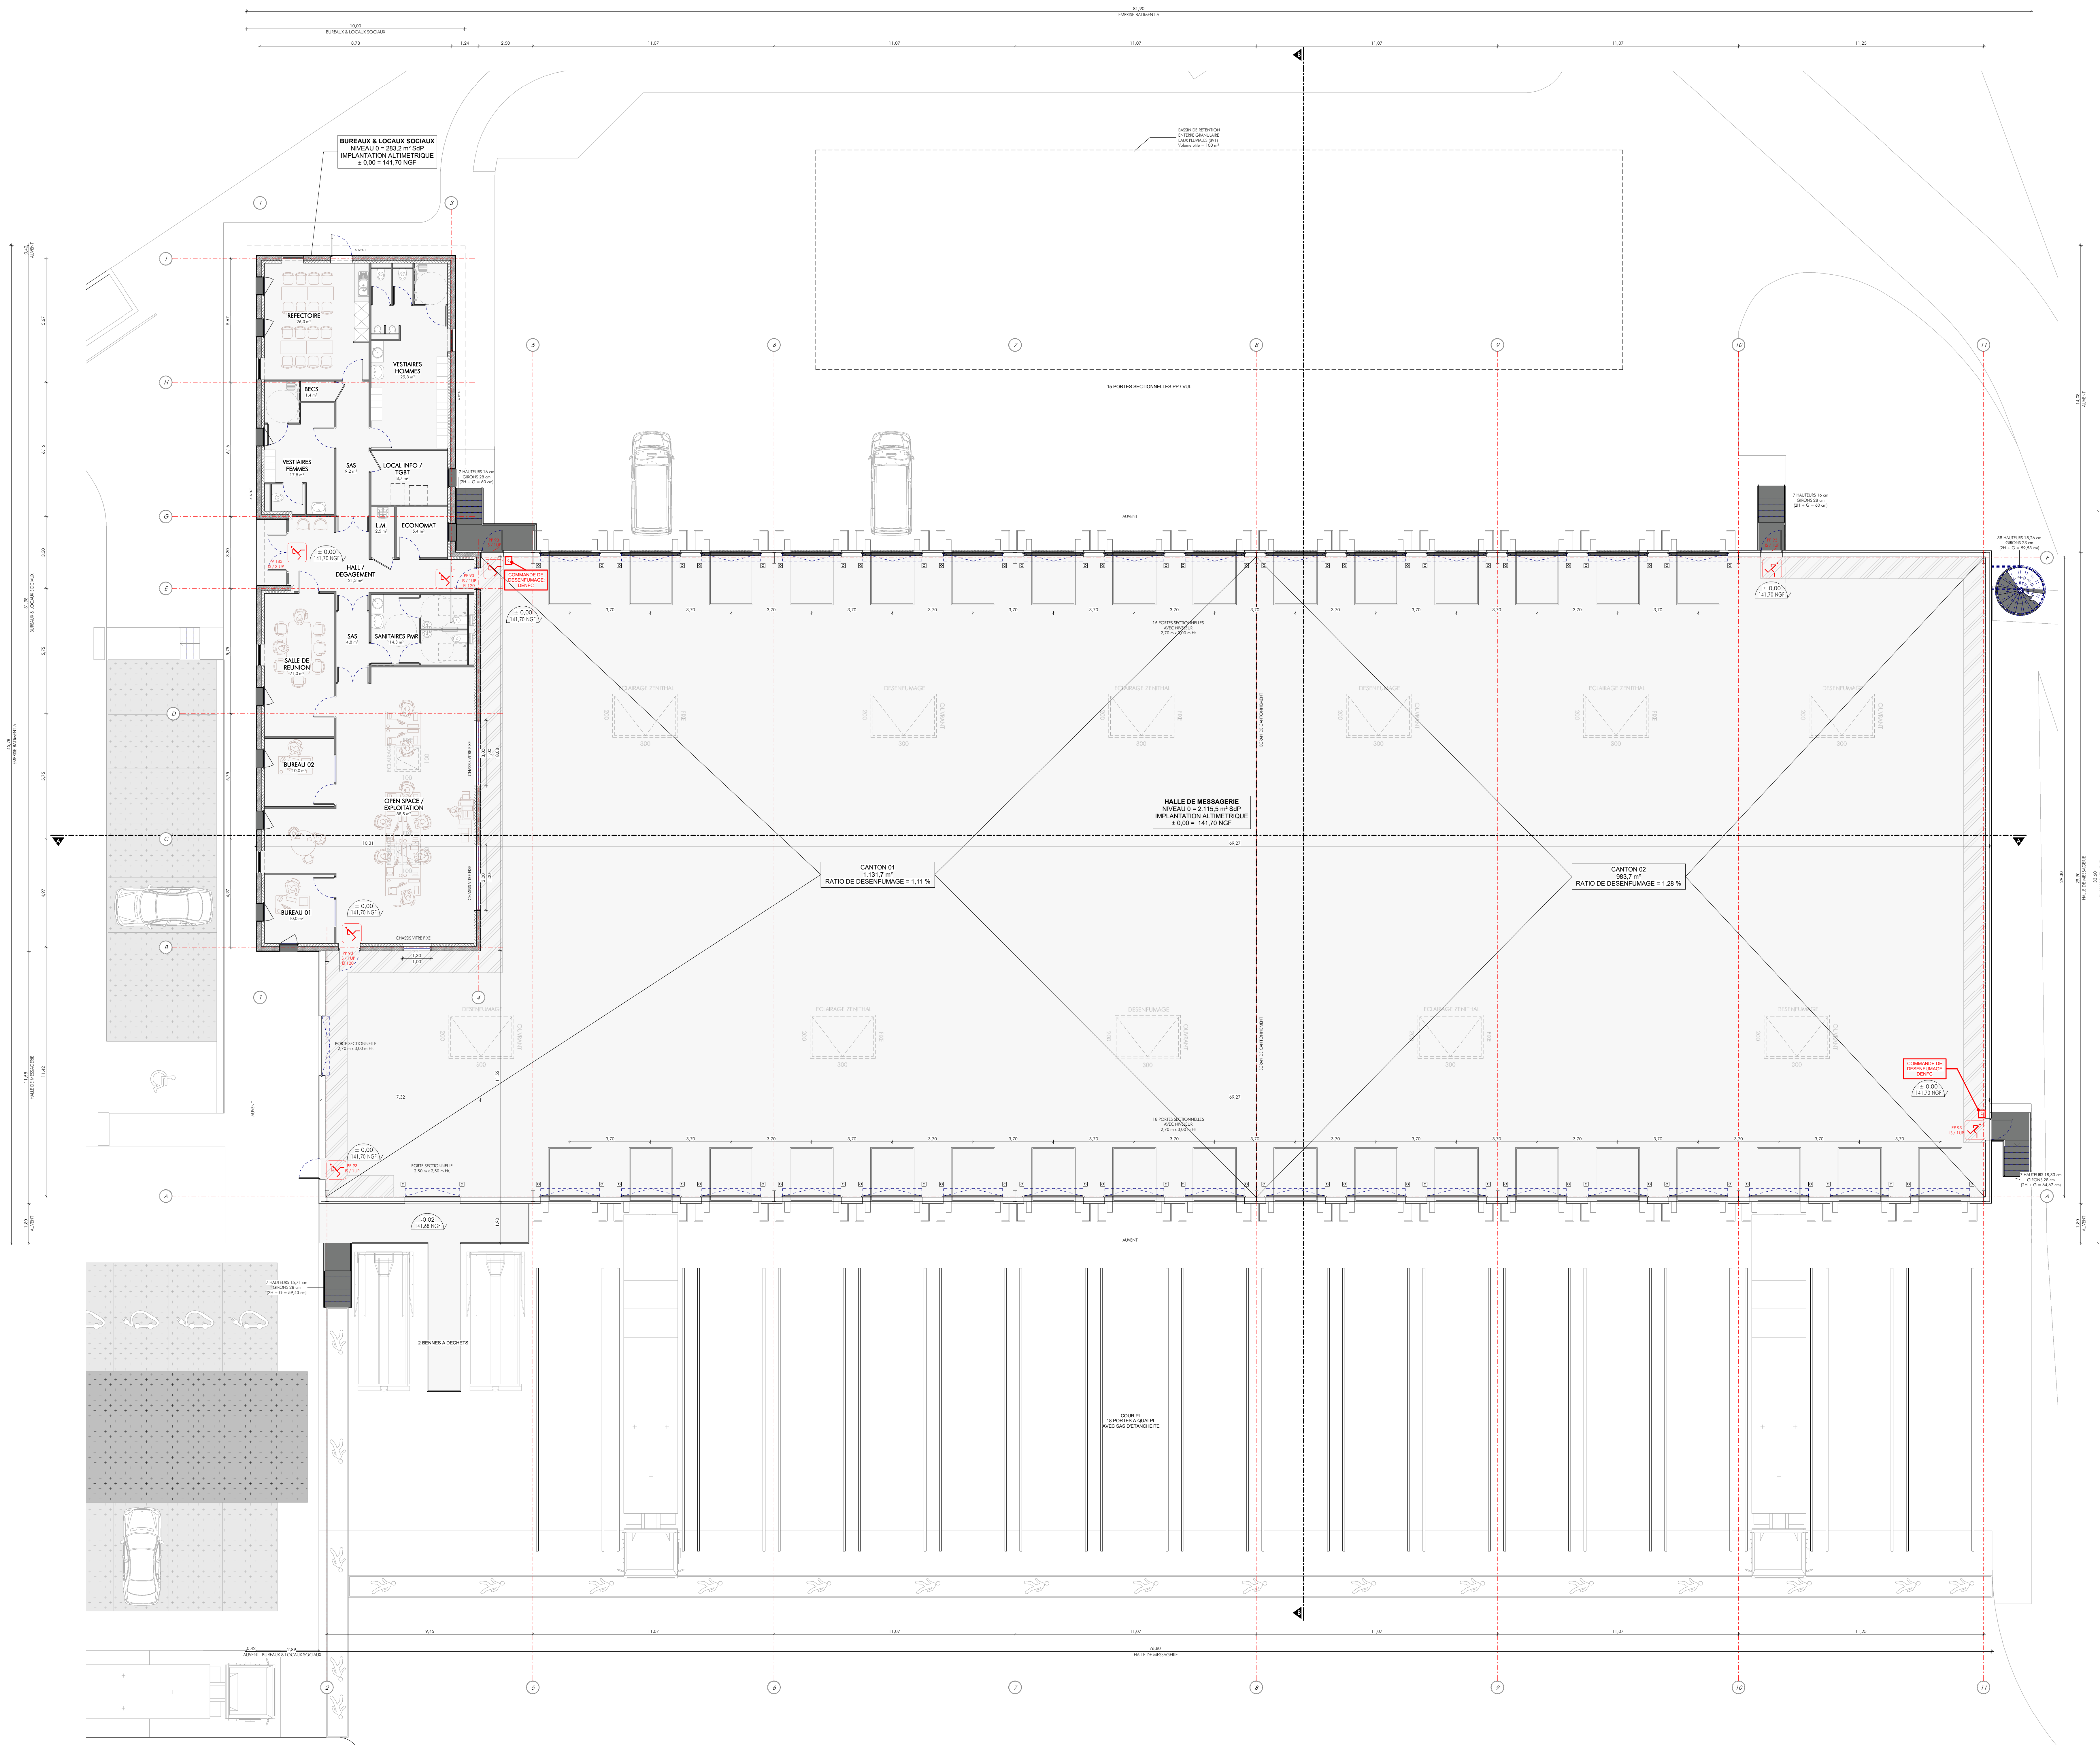

BATIMENT A			
HALLE DE MESSAGERIE	Niveau	Surface Taxable	Surface Plancher
Halle de Distribution	Niveau 0	2 115,5 m ²	2 115,5 m ²
TOTAL HALLE DE MESSAGERIE		2 115,5 m ²	2 115,5 m ²
BUREAUX / LOCAUX SOCIAUX (B.L.S.)			
Bureaux / Locaux Sociaux	Niveau 0	Surface Taxable	Surface Plancher
TOTAL BUREAUX / LOCAUX SOCIAUX (B.L.S.)		283,2 m ²	283,2 m ²
TOTAL NIVEAU 0		2 398,7 m ²	2 398,7 m ²
TOTAL BATIMENT A		2 398,7 m ²	2 398,7 m ²

Soit un Coefficient d'Occupation du Sol de 0,192 sur la parcelle de 12 516,2 m²

NOMS DES BATIMENTS & IMPLANTATIONS ALTIMETRIQUES :

- BATIMENT A : MESSAGERIE ± 0,00 = 141,70 NGF
- BATIMENT B : ABRI DEUX ROUES ± 0,00 = 140,97 NGF
- BATIMENT C : STATION DE LAVAGE ± 0,00 = 141,25 NGF
- BATIMENT D : STATION CARBURANT ± 0,00 = 141,35 NGF

IMPLANTATION ALTIMETRIQUE DE REFERENCE ± 0,00 = 141,70 NGF

BATIMENT A - NIVEAU 0

0996
CAO : KC/PM

V15

03

1/100ème
Revit 2024

0996-V15-GENERAL.rvt

GEODIS D&E ARMORIQUE

CONSTRUCTION D'UNE MESSAGERIE

ZAE DU GOHELIS - ILOT E

56250 ELVEN

MISE A JOUR DE PLANS DE DEMANDE DE PERMIS DE CONSTRUIRE
30 SEPTEMBRE 2025

DEMANDEUR
GEODIS D&E ARMORIQUE
25 Quai Charles Perret
92300 LEVALLOIS-PERRET
+33 (0)1 46 46 25 56
christophe.grisot@geodis.com

ARCHITECTE
S.A.R.L. d'architecture ARCH-FACTORY
Espace du Tor
13, Boulevard Jean Monnet
92080 LAMORILLAGE
+33 (0)2 97 35 08 80
Contact@arch-factory.eu

GEODIS

ARCH-FACTORY