



COUPE LONGITUDINALE A-A

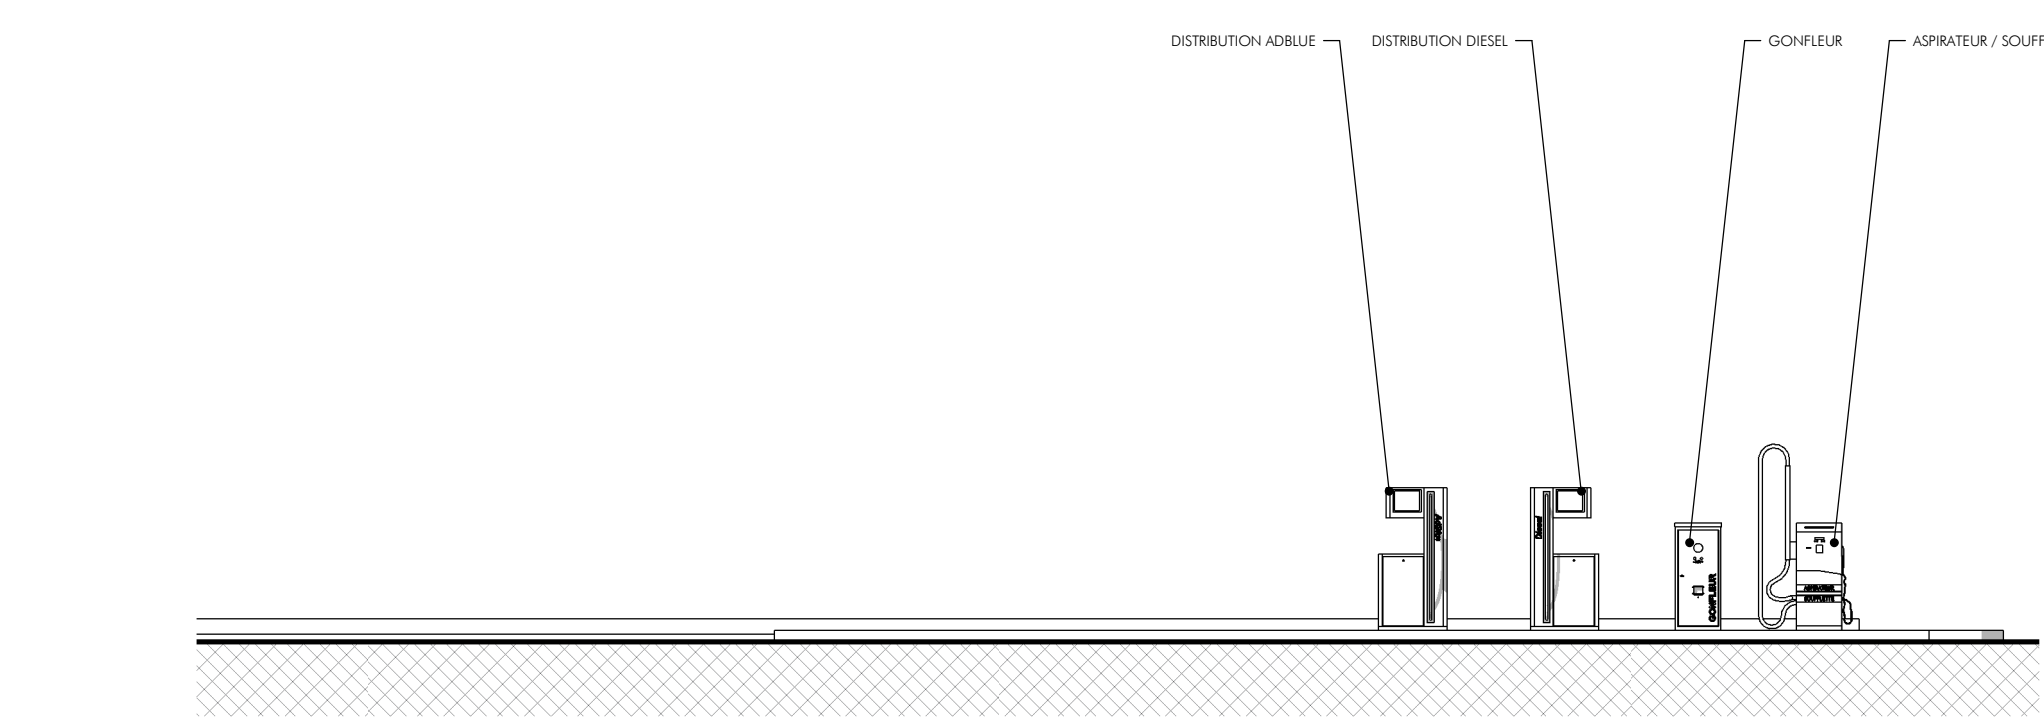


COUPE SUR STATION

COUPES

FACADES

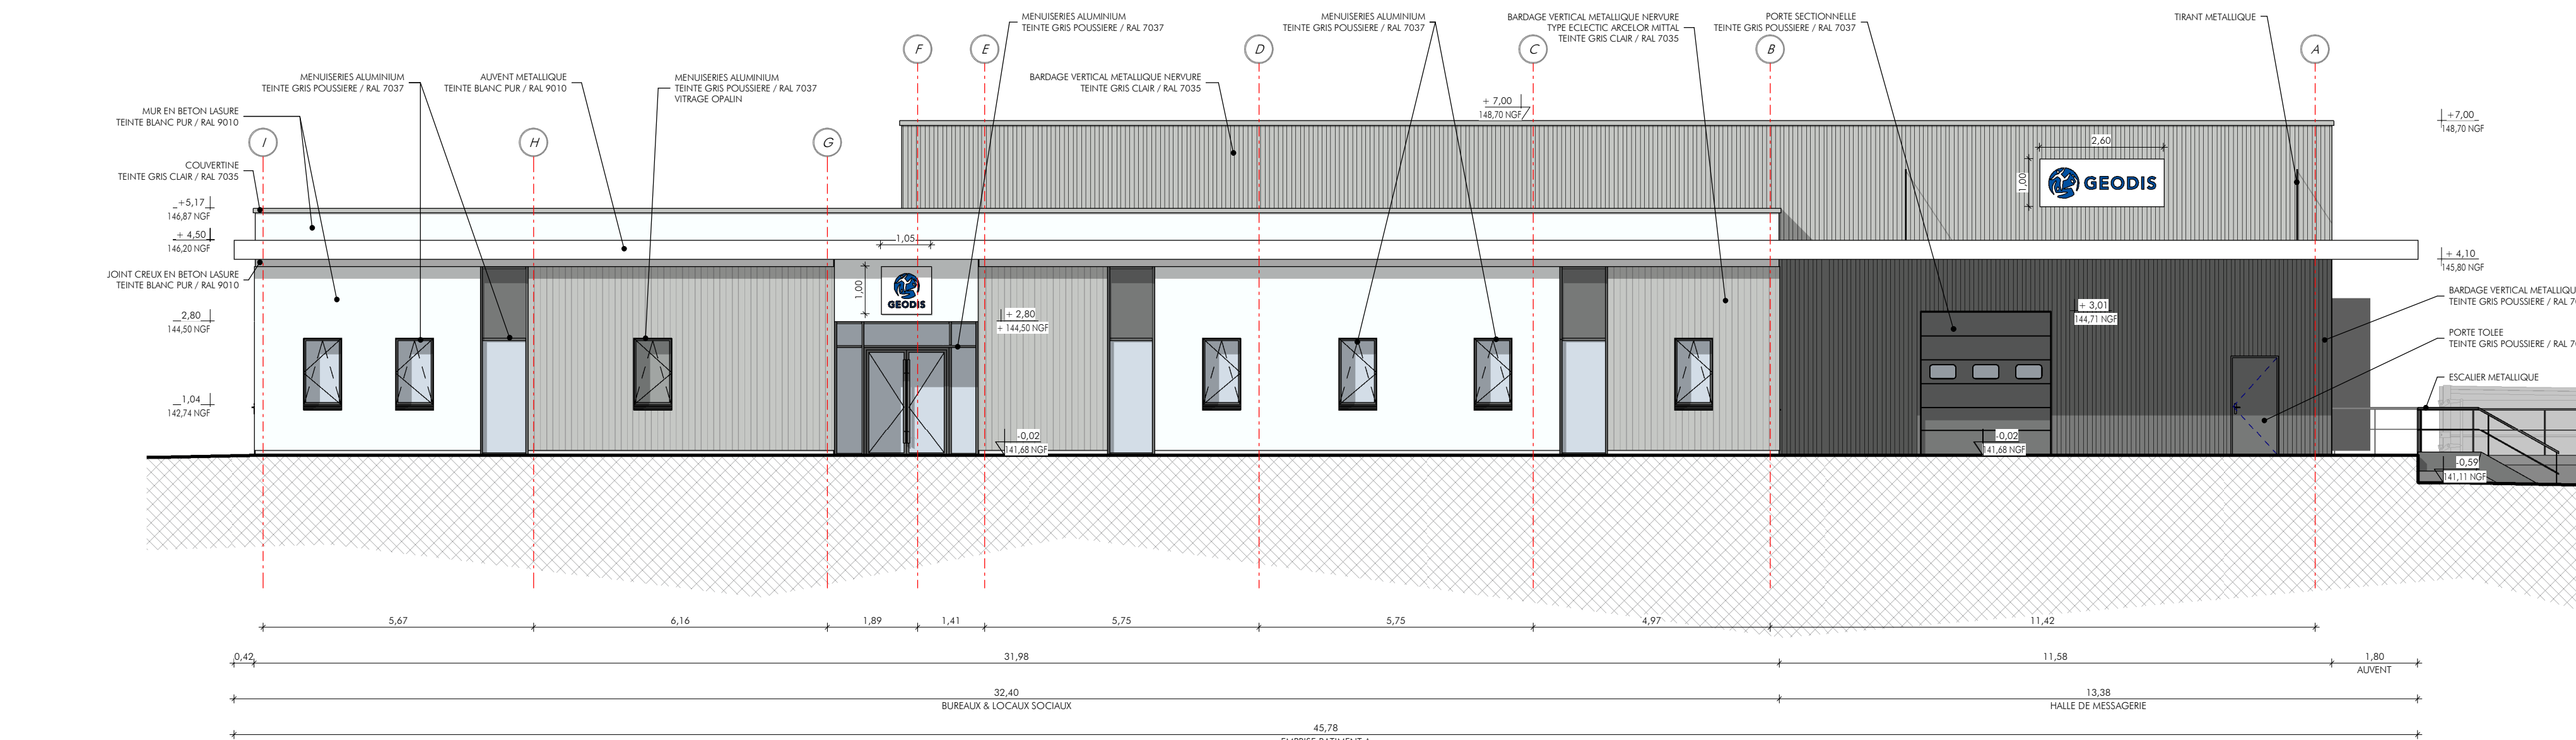


FACADE OUEST

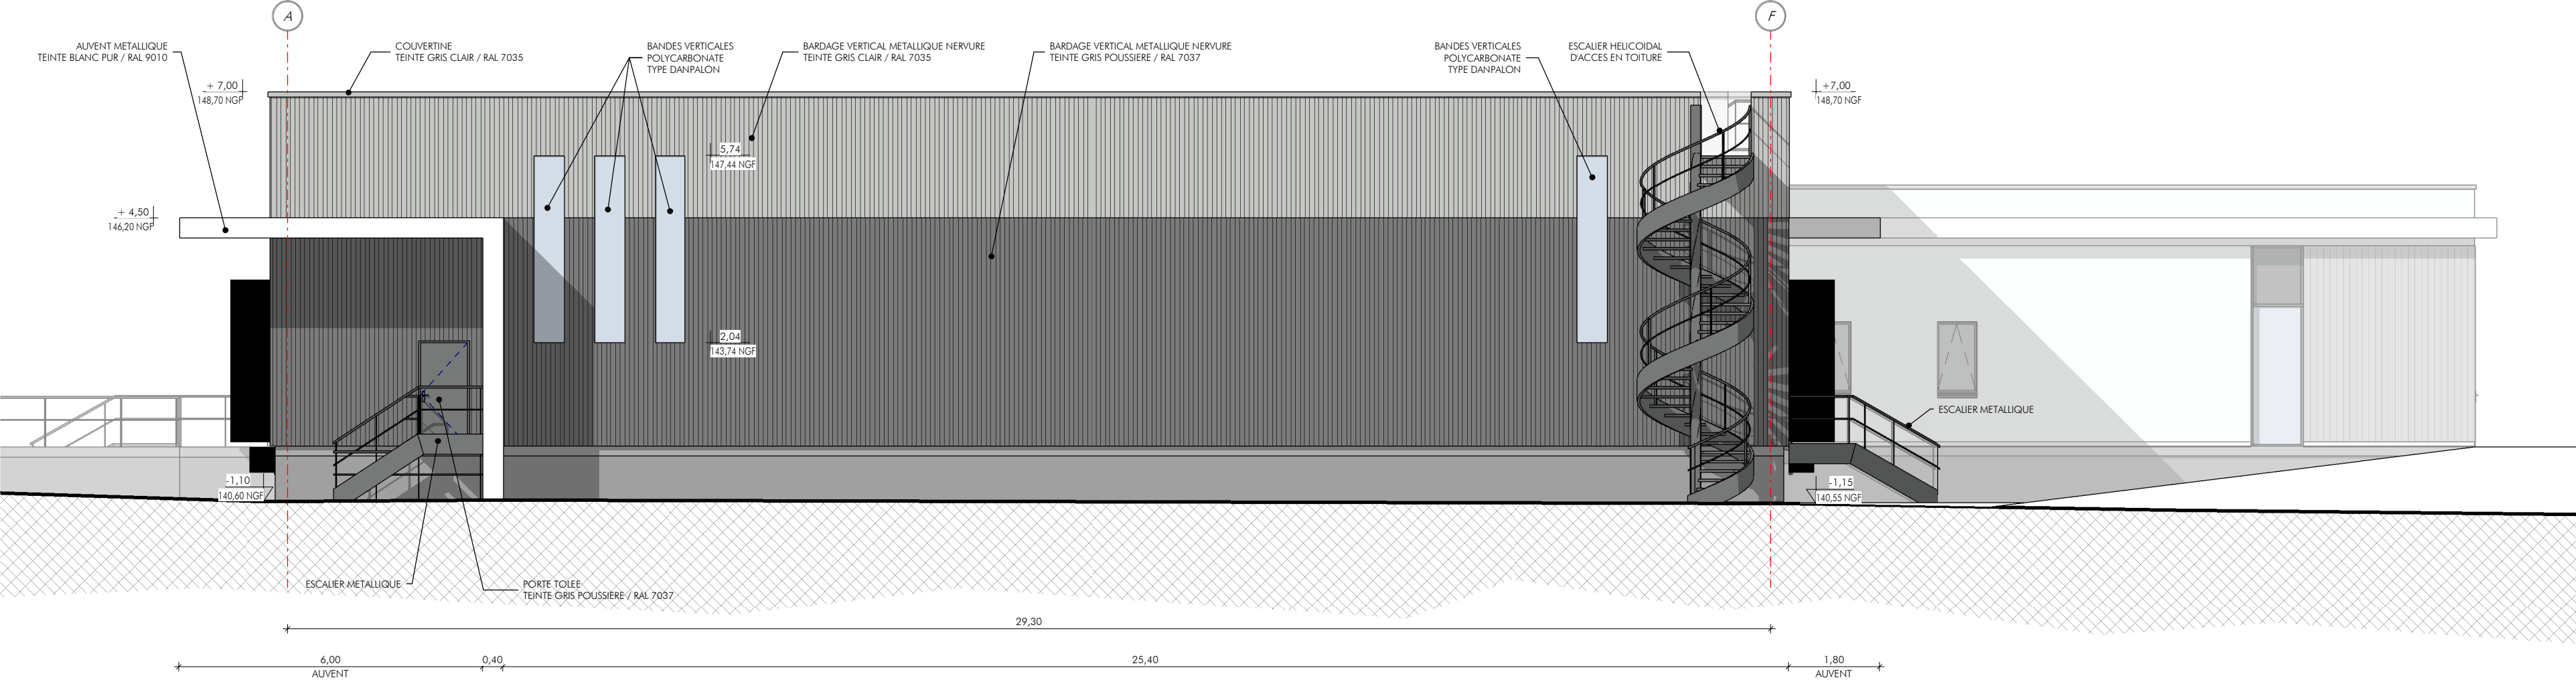


FACADE NORD-EST


FACADE NORD-EST

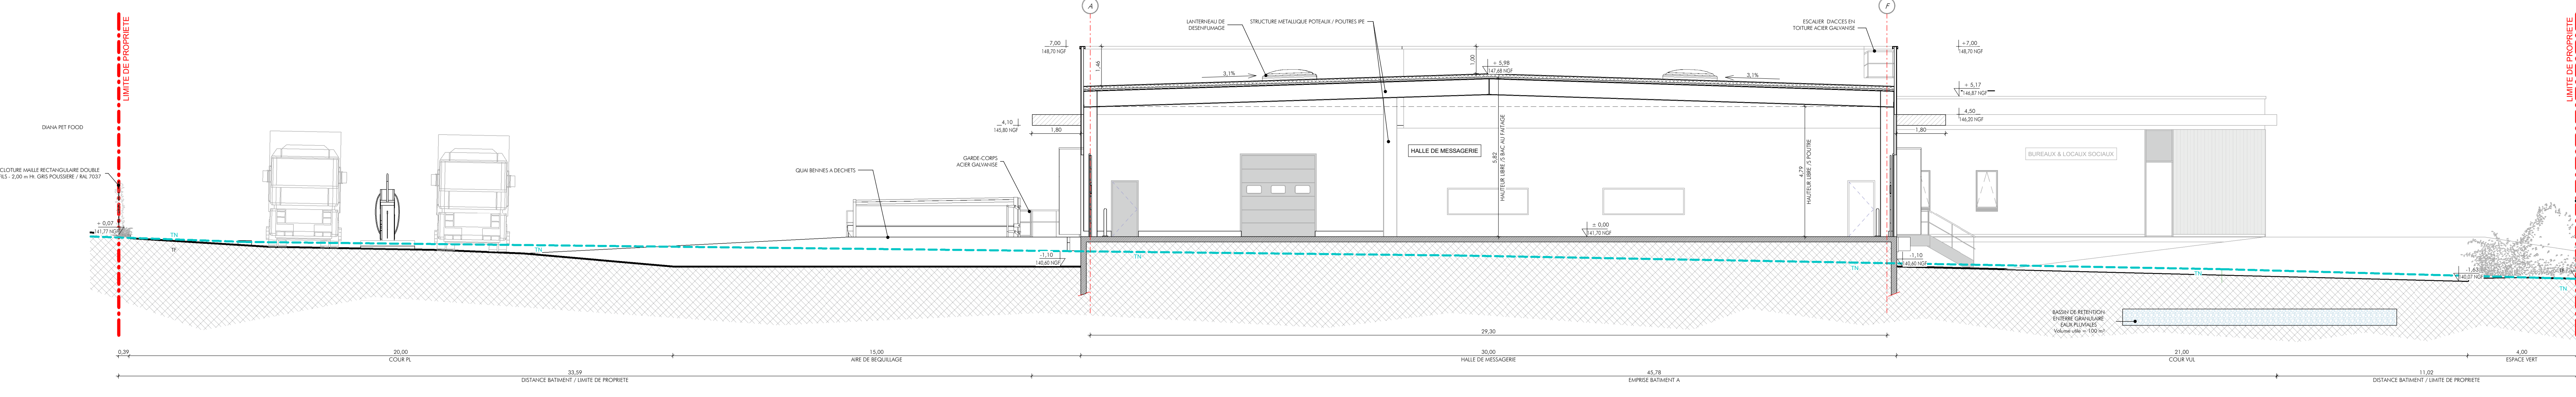

COUPE TRANSVERSALE B-B

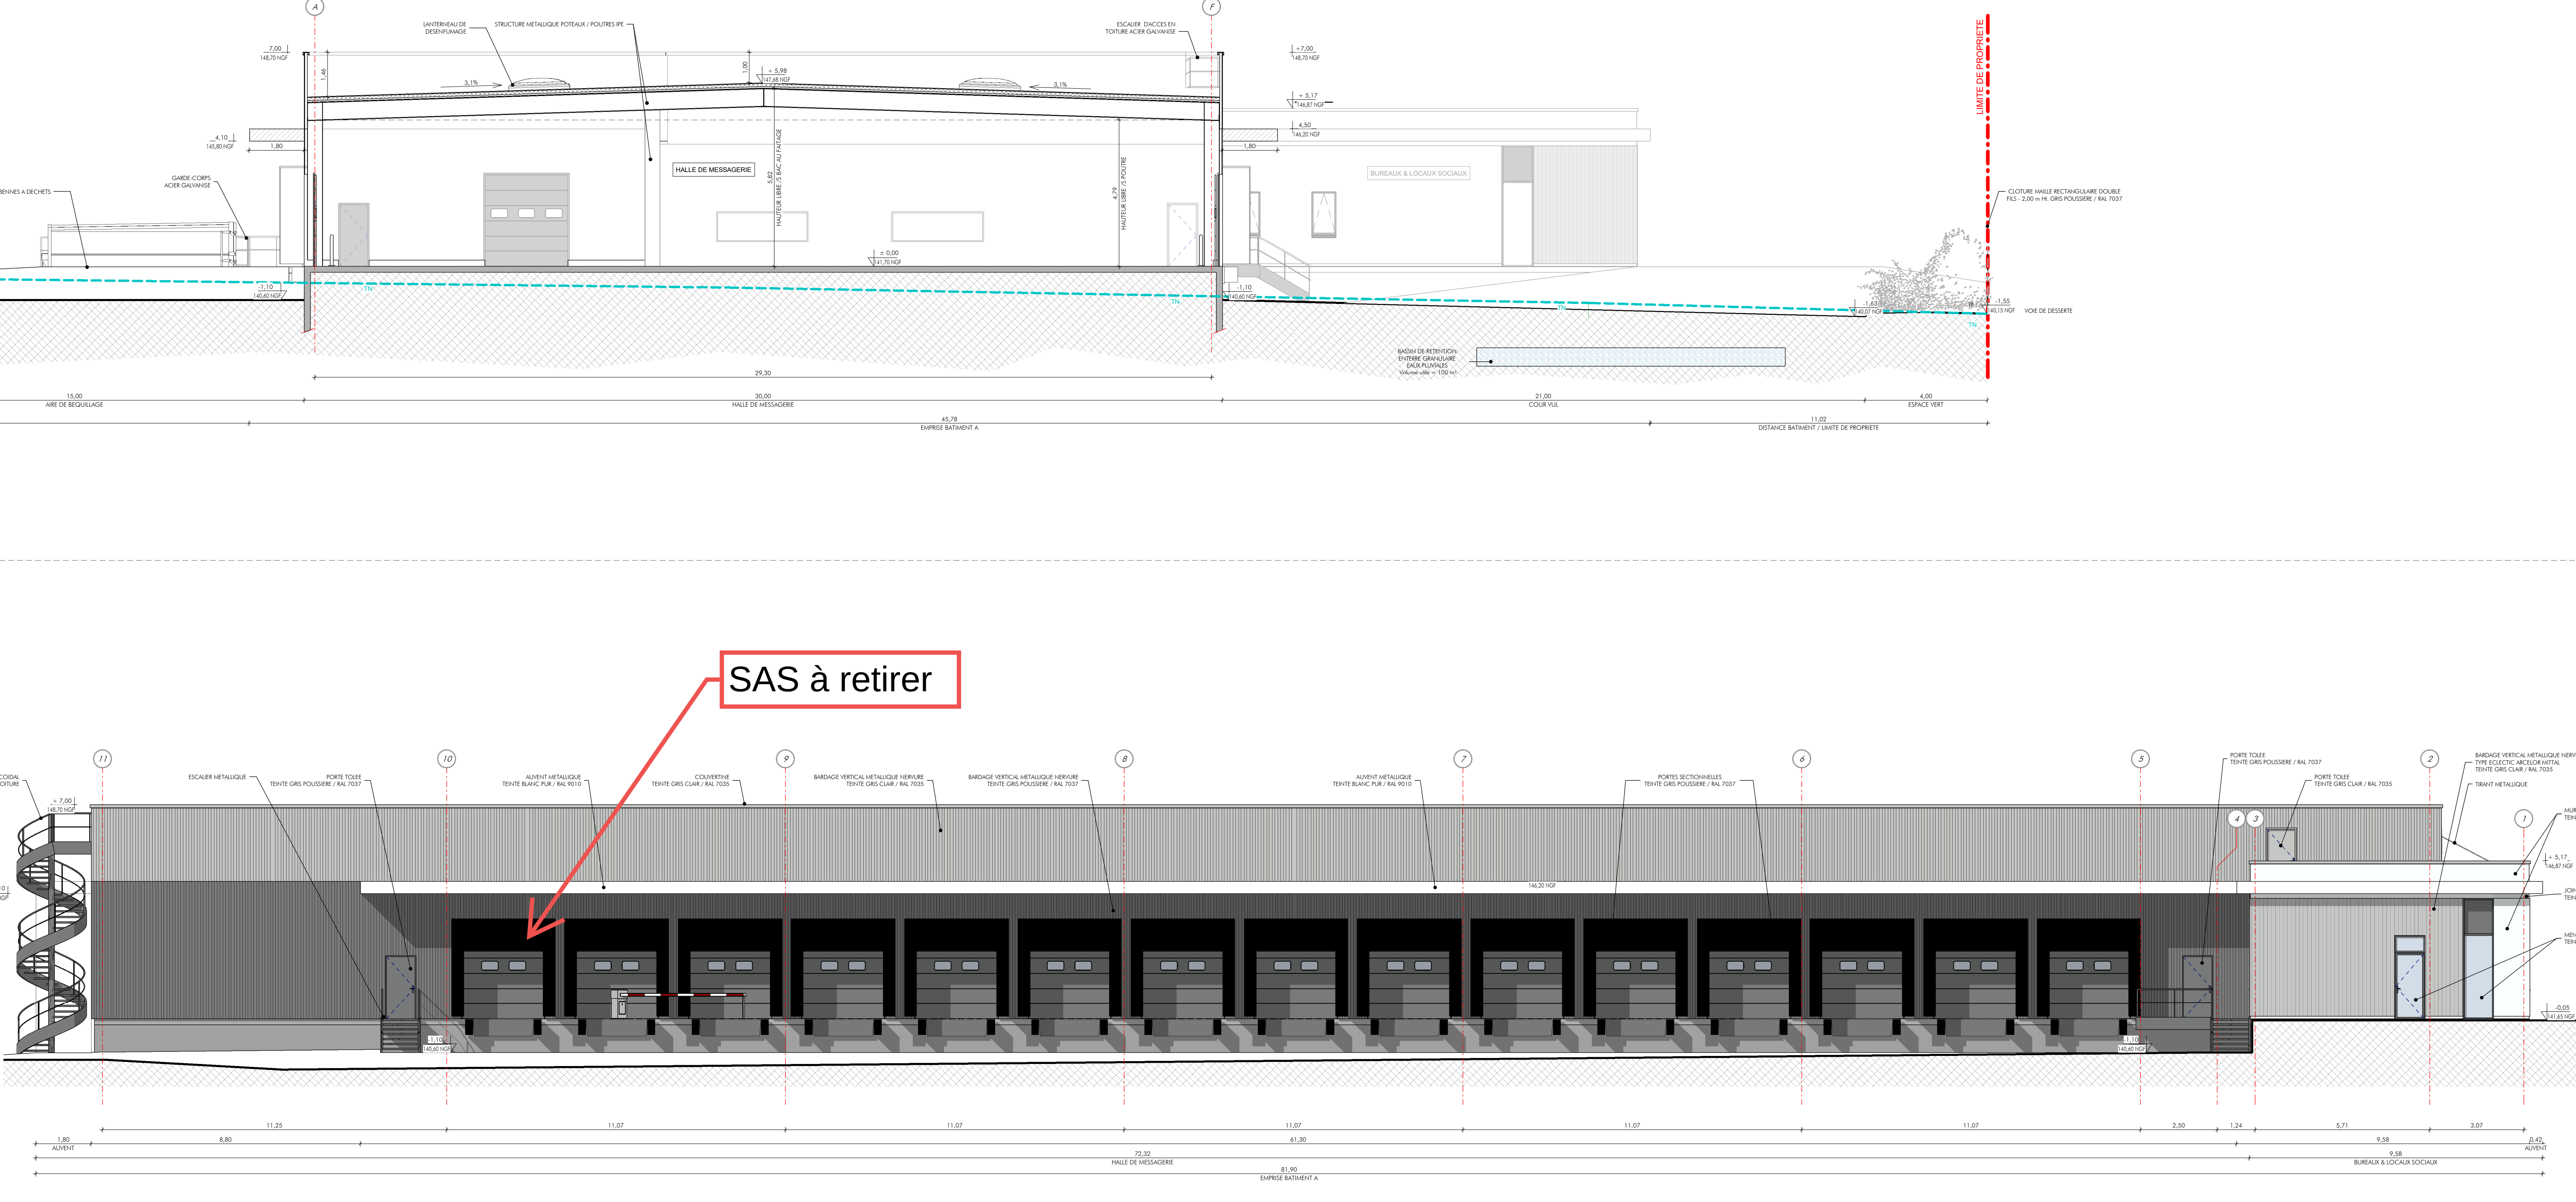


FACADE NORD-OUEST

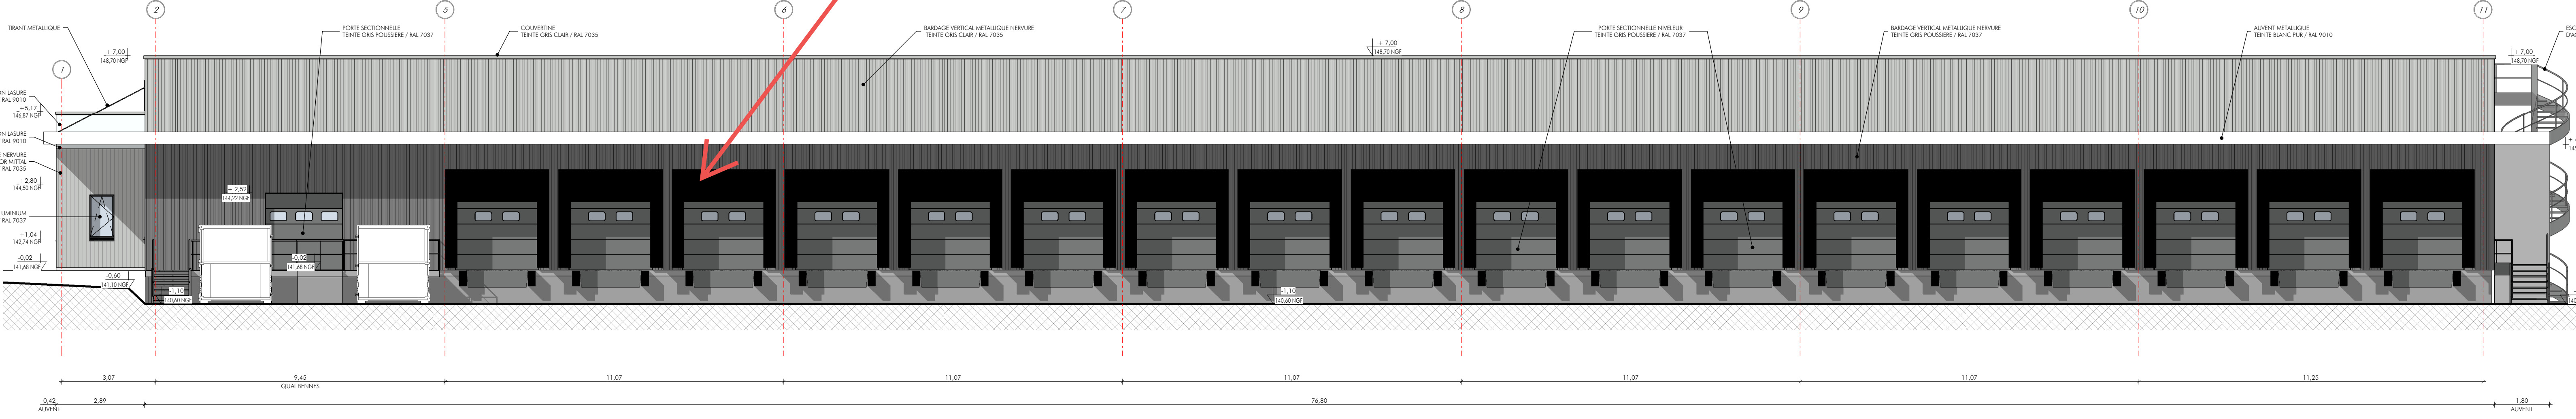

FACADE SUD-EST

FACADE SUD-EST

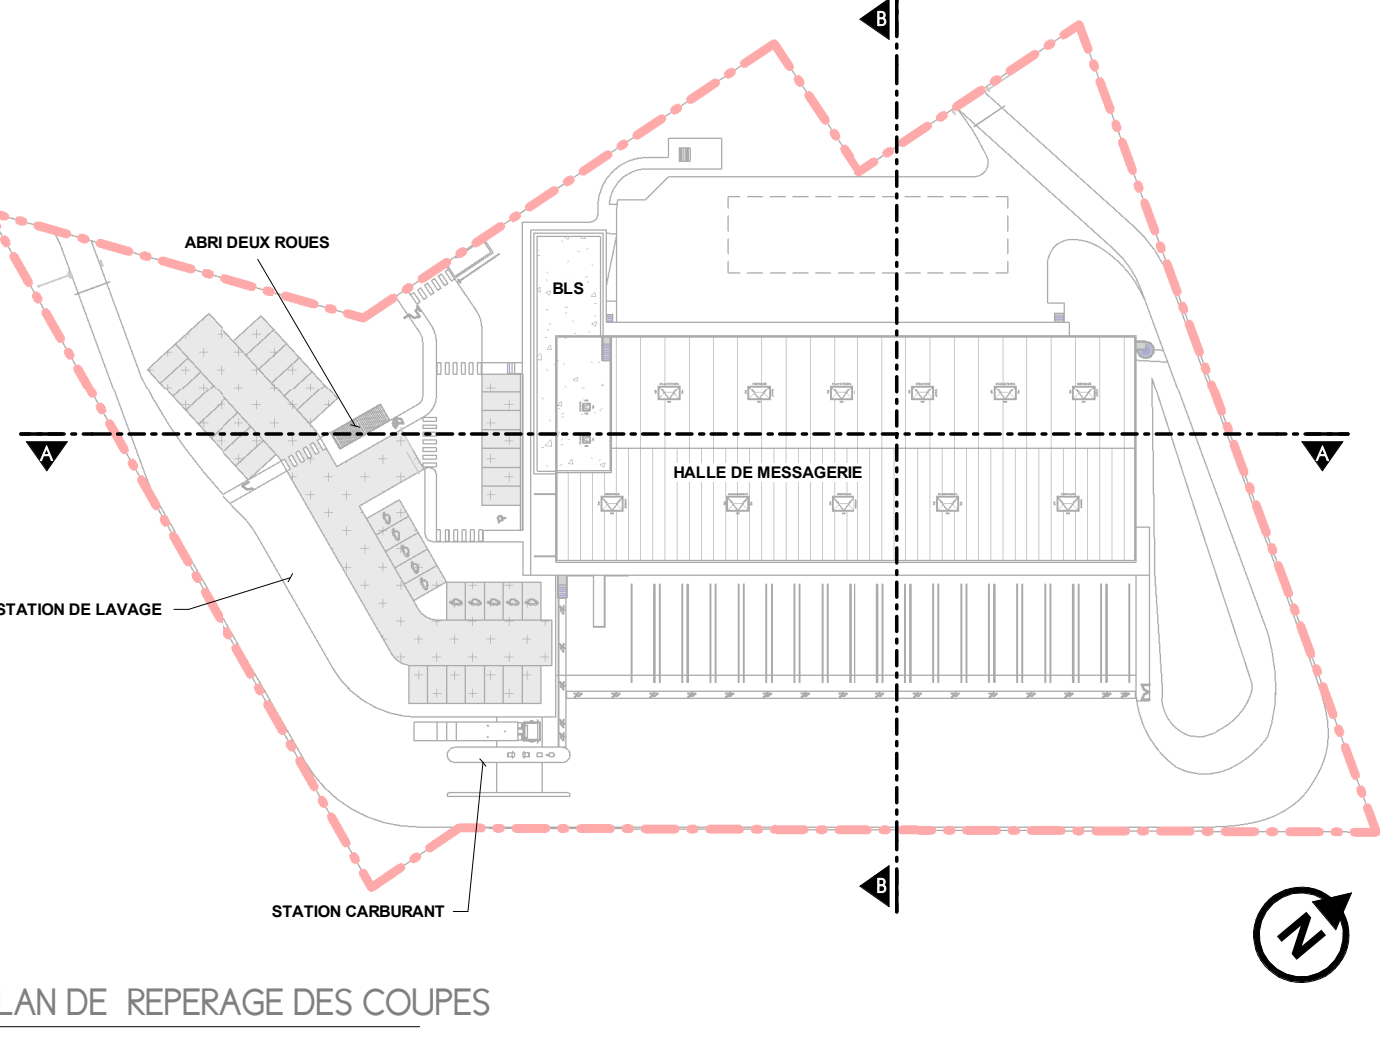

PLAN DE REPERAGE DES COUPES

NOMS DES BATIMENTS & IMPLANTATIONS ALTIMETRIQUES :	
- BATIMENT A : MESSAGERIE	± 0.00 = 141.70 NGF
- BATIMENT B : ATRI DEUX ROUES	± 0.00 = 140.97 NGF
- BATIMENT C : STATION DE LAVAGE	± 0.00 = 141.25 NGF
- BATIMENT D : STATION CARBURANT	± 0.00 = 141.35 NGF
IMPLANTATION ALTIMETRIQUE DE REFERENCE ± 0.00 = 141.70 NGF	

BATIMENT A - FACADES & COUPES

05

0295
CAO : K.C.P.N.N
0998 : VIS - GENERAL.rvt

1/100ème
Revue 2024

PIECE PCM 05

GEODIS D&E ARMORIQUE
CONSTRUCTION D'UNE MESSAGERIE
ZAE DU GHELIS - LOT E
56250 ELVEN

PROVISOIRE

DEMANDEUR
GEODIS D&E ARMORIQUE
20 Quai Charles Pasteur
92000 LEVALLOIS PERRET
+33 (0) 1 46 46 25 88
christophe.greiner@gedis.com

ARCHITECTE
S.A.R.L. d'architecture ARCH-FACTORY
13 Boulevard Jean Monnet
92000 LEVALLOIS PERRET
+33 (0) 1 46 46 25 88
Contact@arch-factory.eu

MISE EN ŒUVRE DE LA CONSTRUCTION
D'UN PERMIS DE CONSTRUCTION
30 SEPTEMBRE 2025